
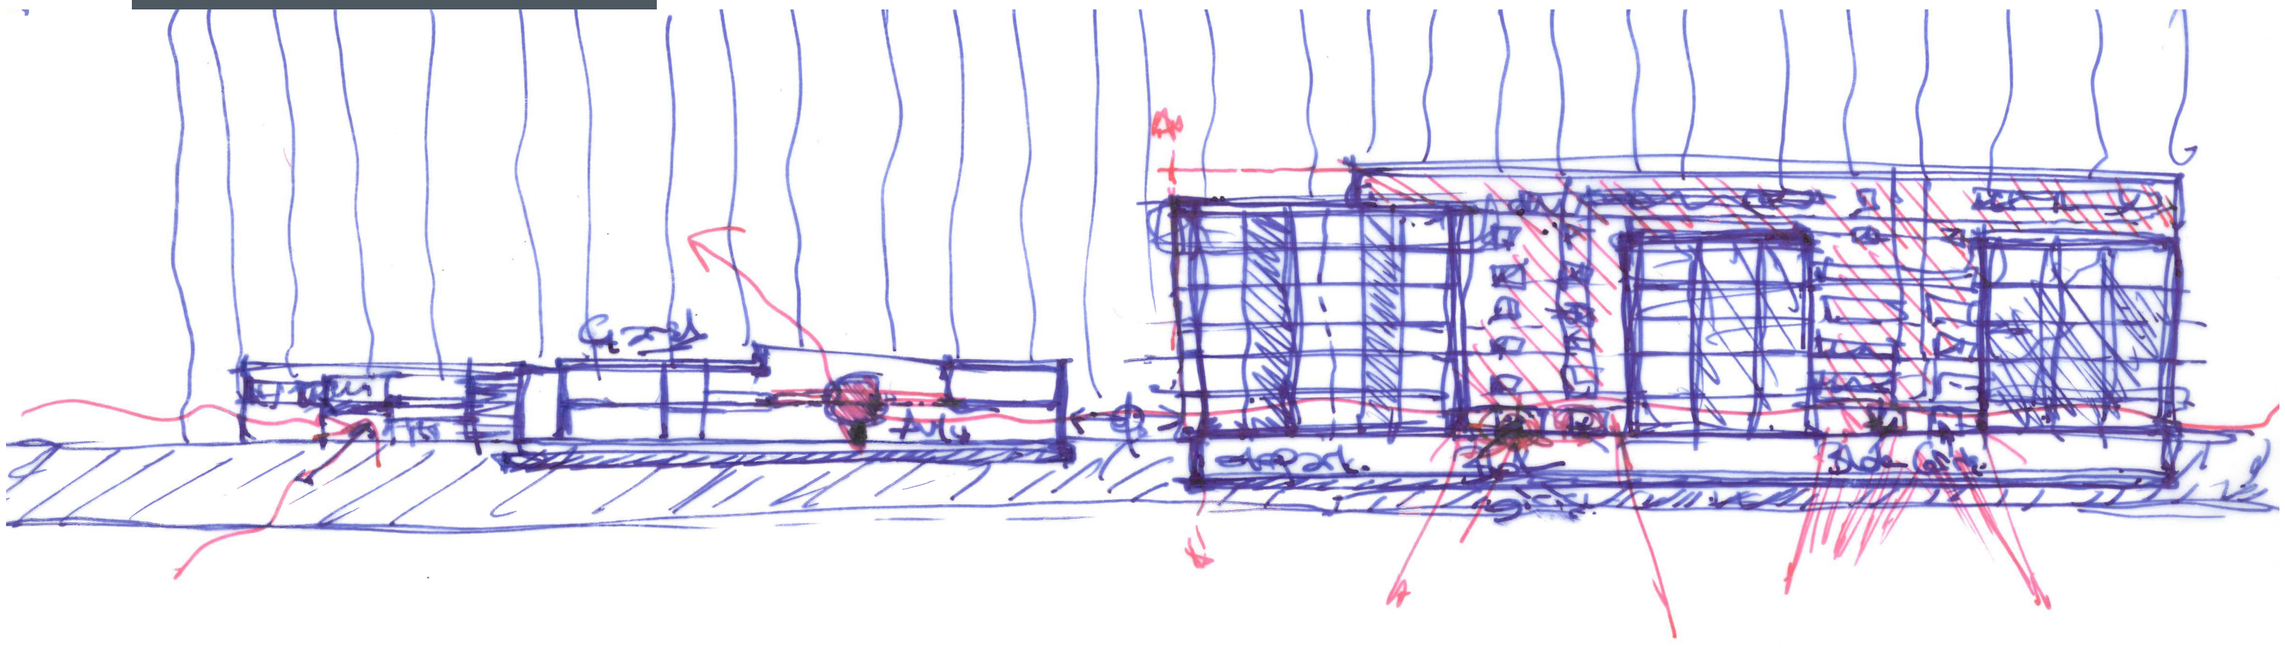


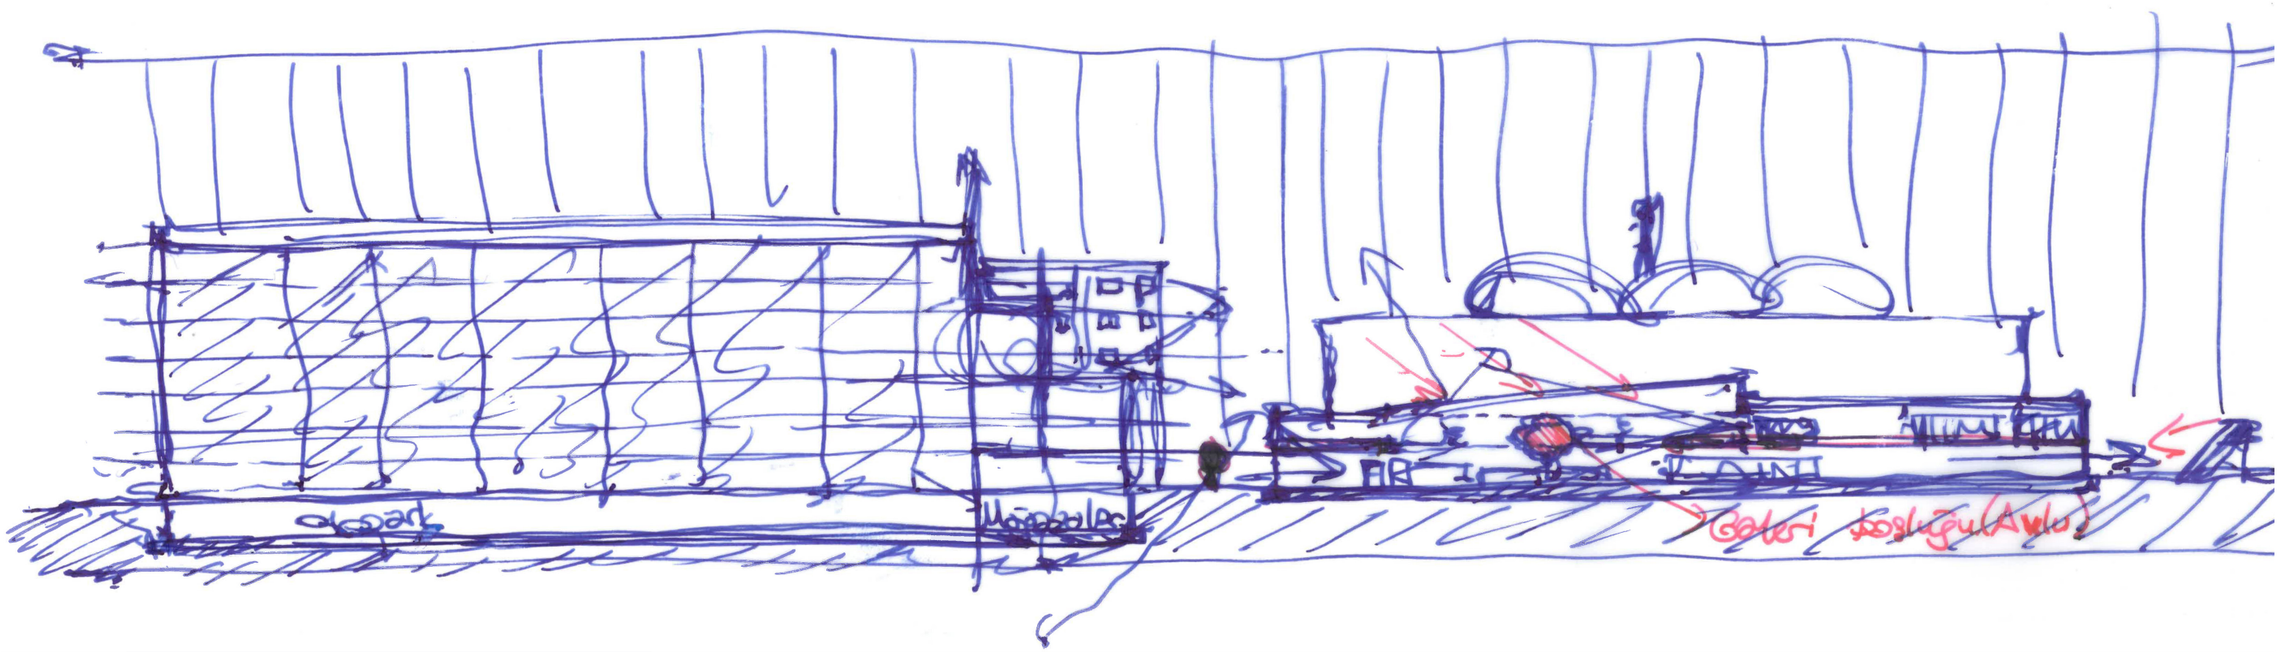

Conceptual Section Studies

These conceptual section sketches explore the massing and floor-level relationships between the residential blocks, highlighting the internal courtyard and gallery spaces within the commercial unit, as well as building entrances, circulation routes and spatial transitions.