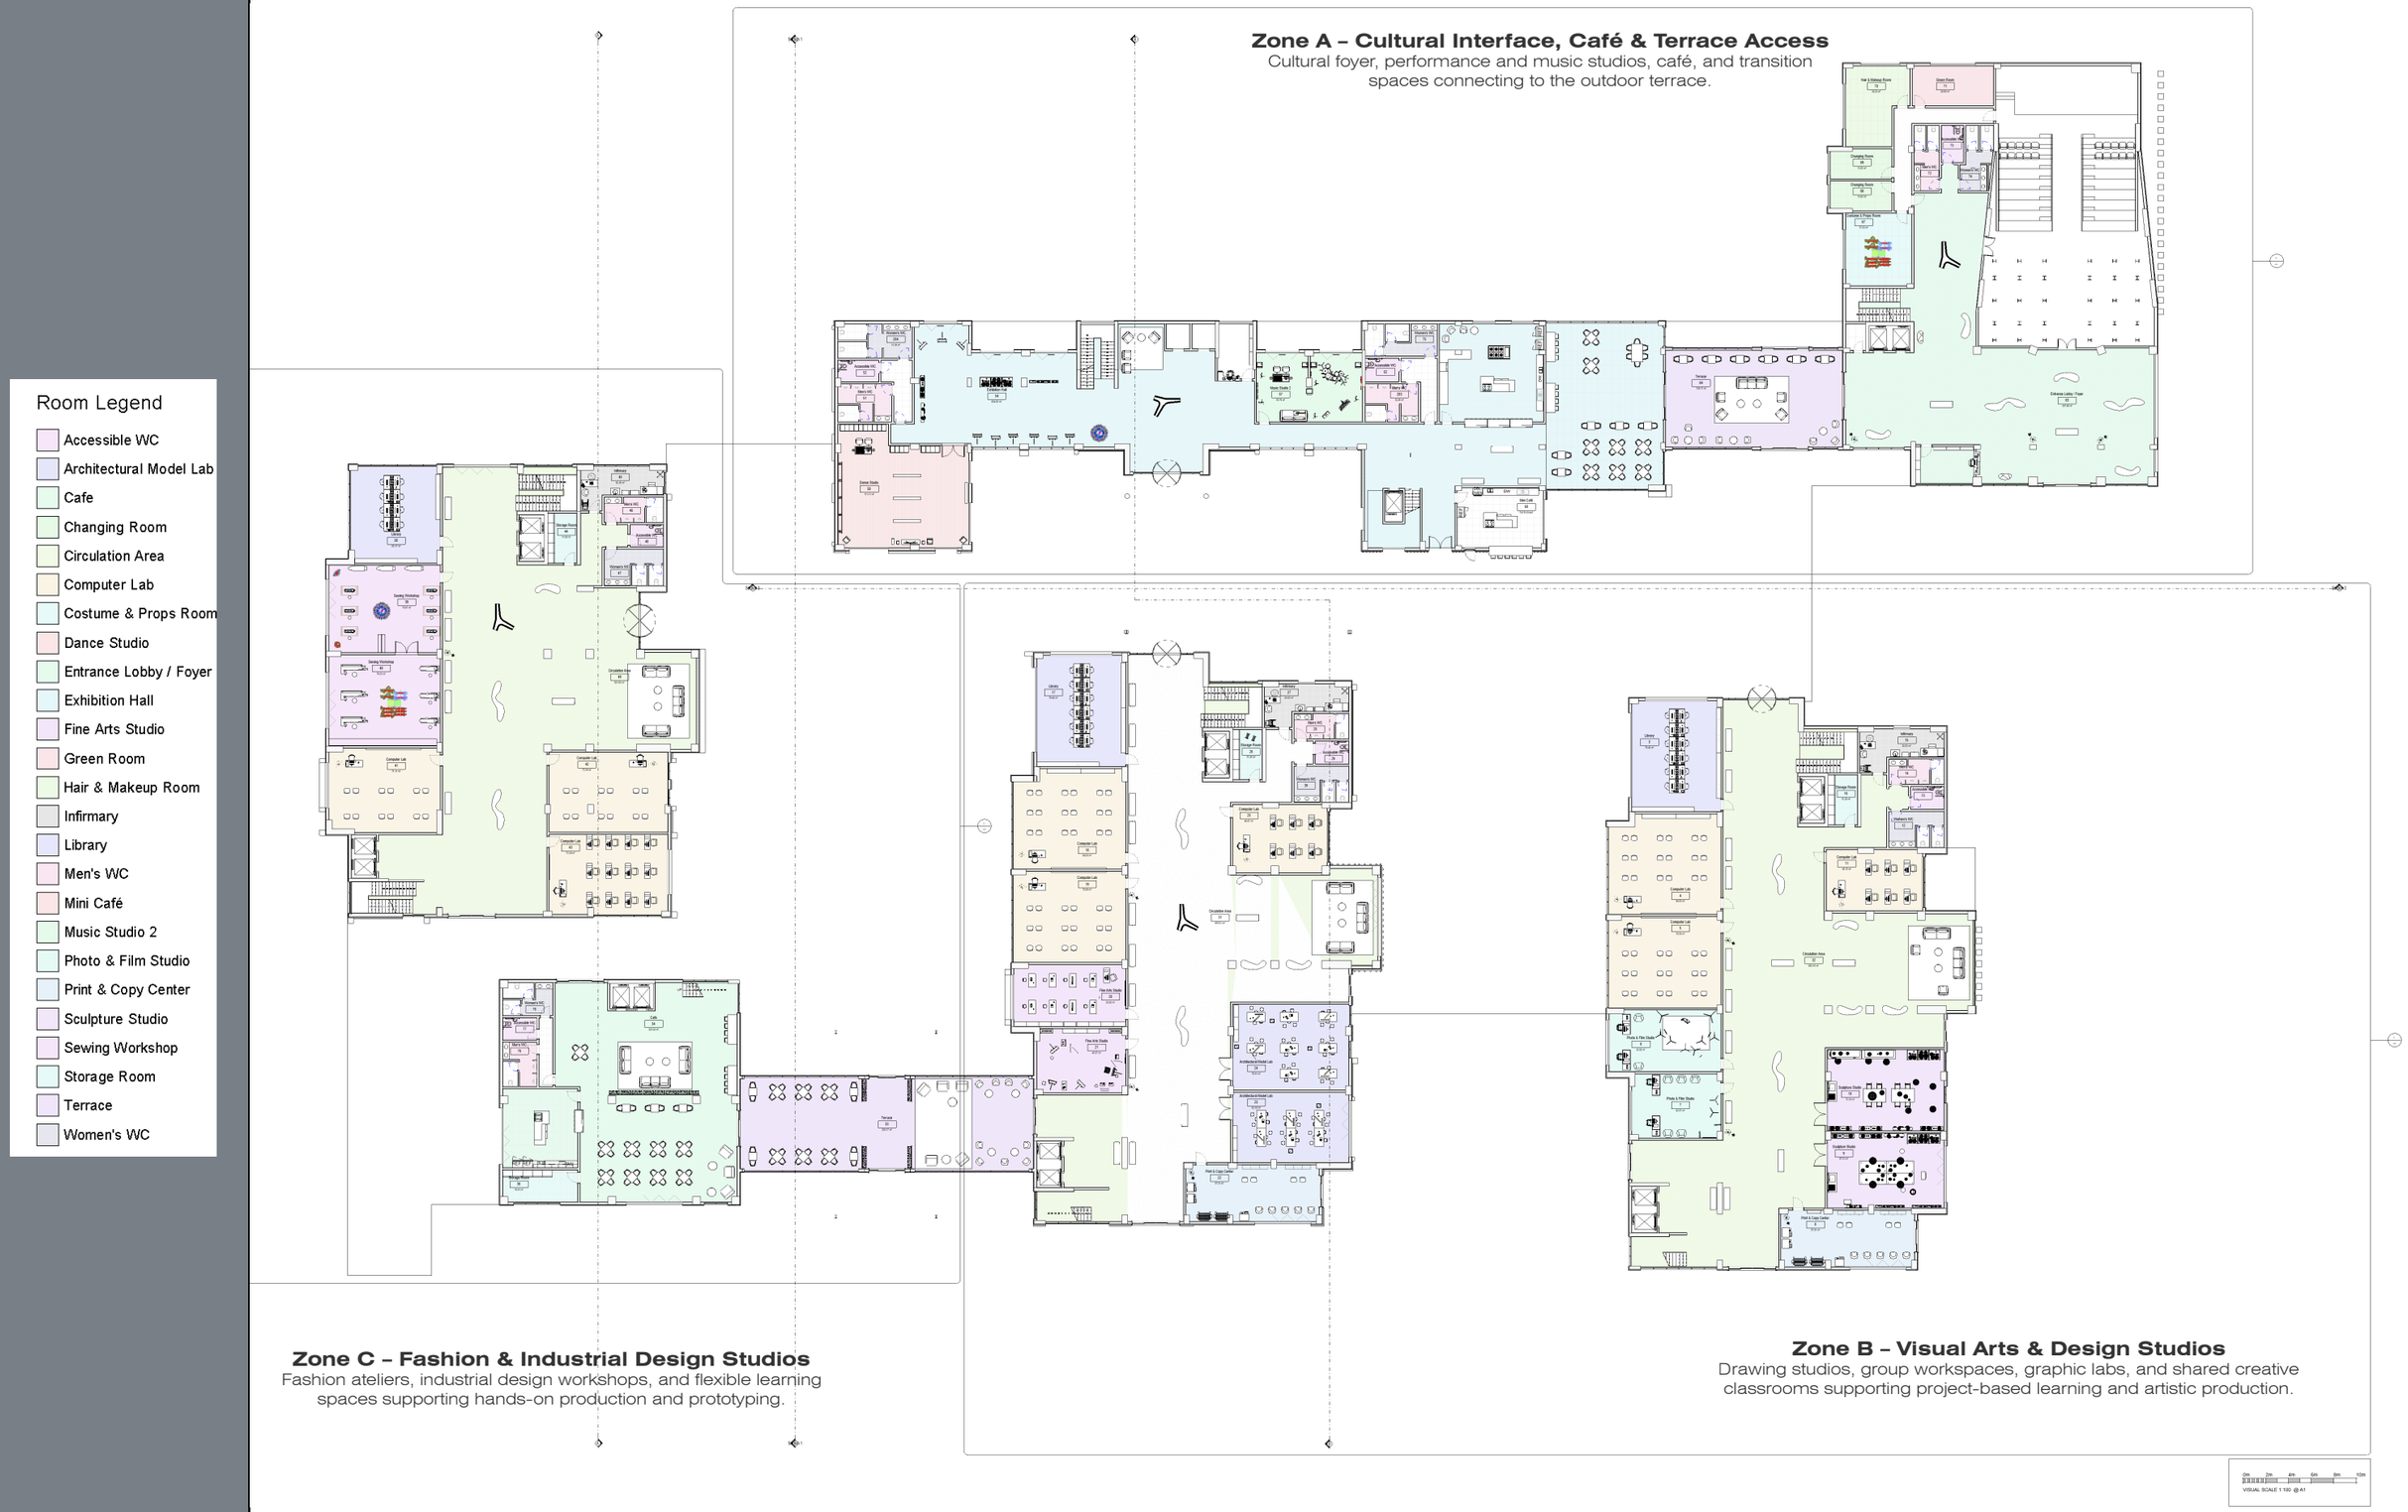


Ground Floor Plan | Scale: NTS

Shows spatial organization, public interfaces, and internal distribution on the ground level.