
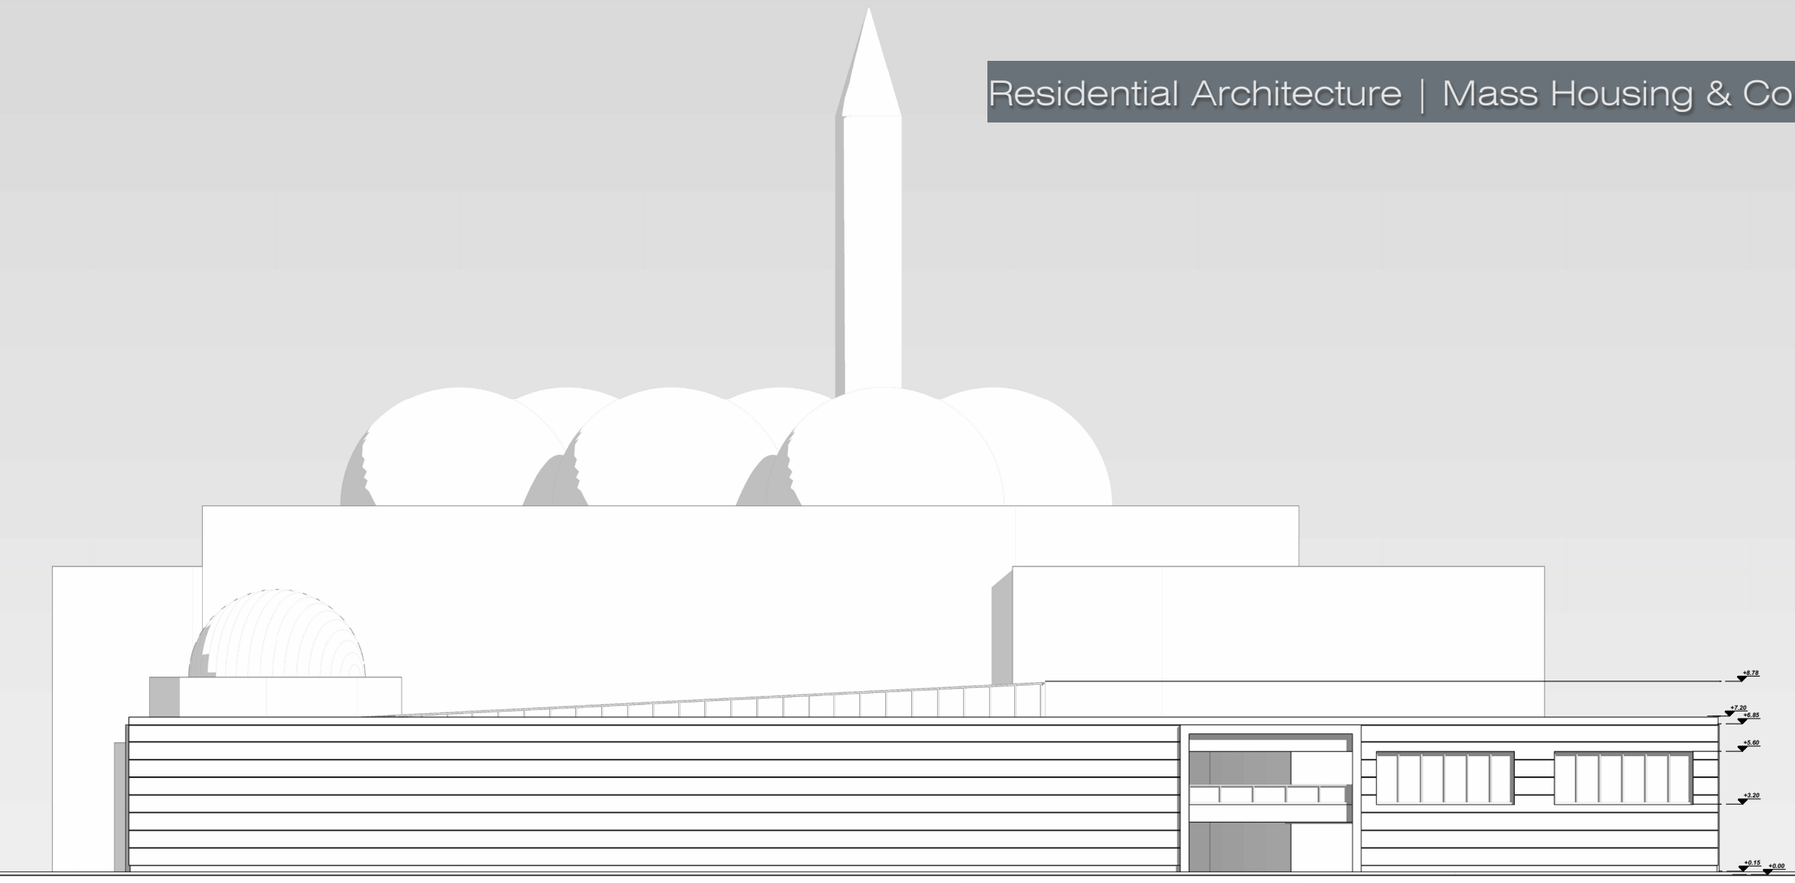


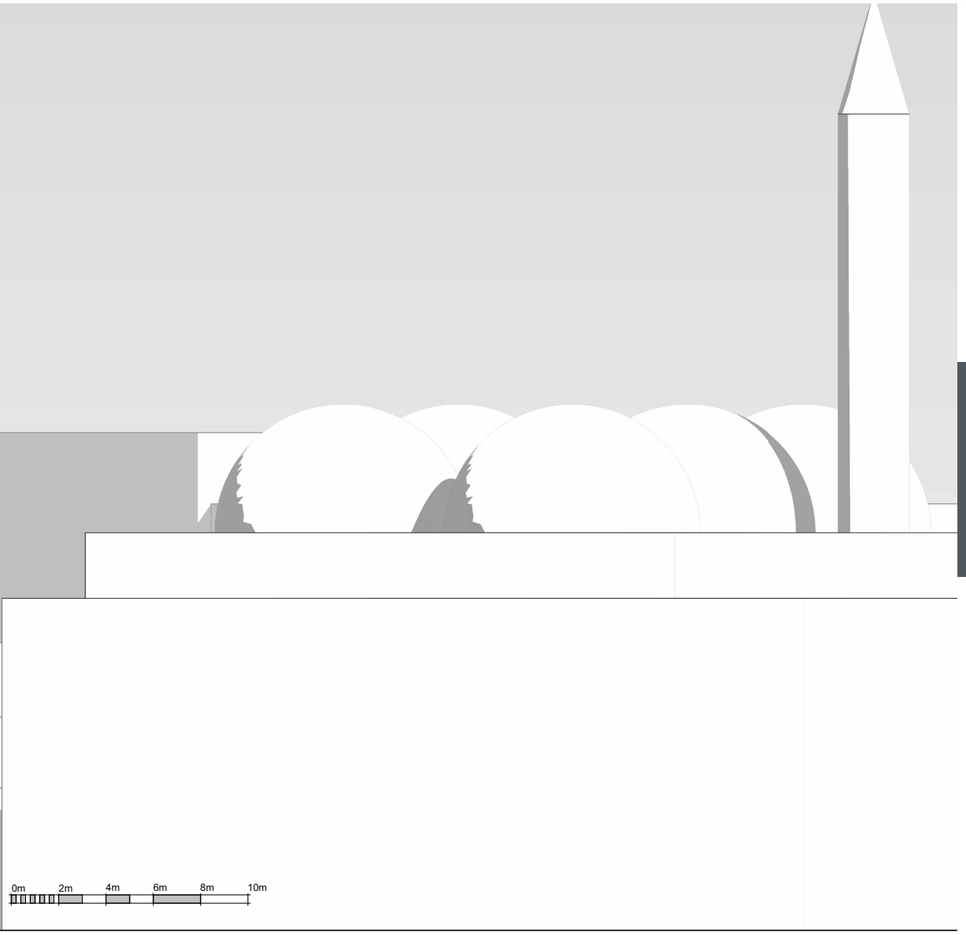

Architectural Elevations | Scale: NTS

Elevation studies illustrating the relationship between residential blocks of varying heights, commercial frontage, and the surrounding urban context.