


SECTION 2-2

Sections

The sections illustrate the relationship between the housing clusters, changing building heights and the surrounding ground levels.
They also reveal the internal spatial organization of the residential blocks and their connection with the shared outdoor spaces.

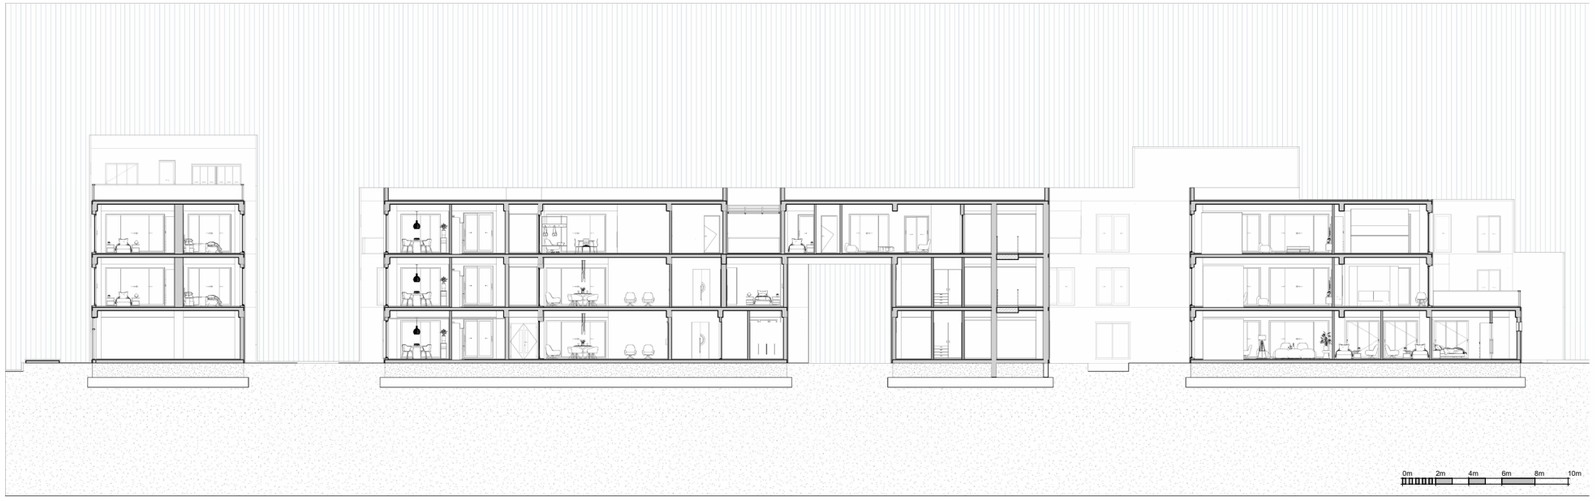

SECTION 1-1